New final escape and BOH doors by tenant.
Performance:
Acoustics Rw40
Fire 60FDS
(Final escape door to have glazed vision panels)


Tenant confirm lobby layout with open layout to WC's agreed with BC

Lobby escape doors by tenant.
Performance:
Acoustics Rw30
Fire 60FDS

Tenant to confirm:
S/O door required

New final escape and lobby escape doors by tenant.
Performance:
Acoustics Rw30
Fire 60FDS
(Final escape door to have glazed vision panels)

Tenant to confirm:
S/O door required
Confirm lobby depth agreed by BC

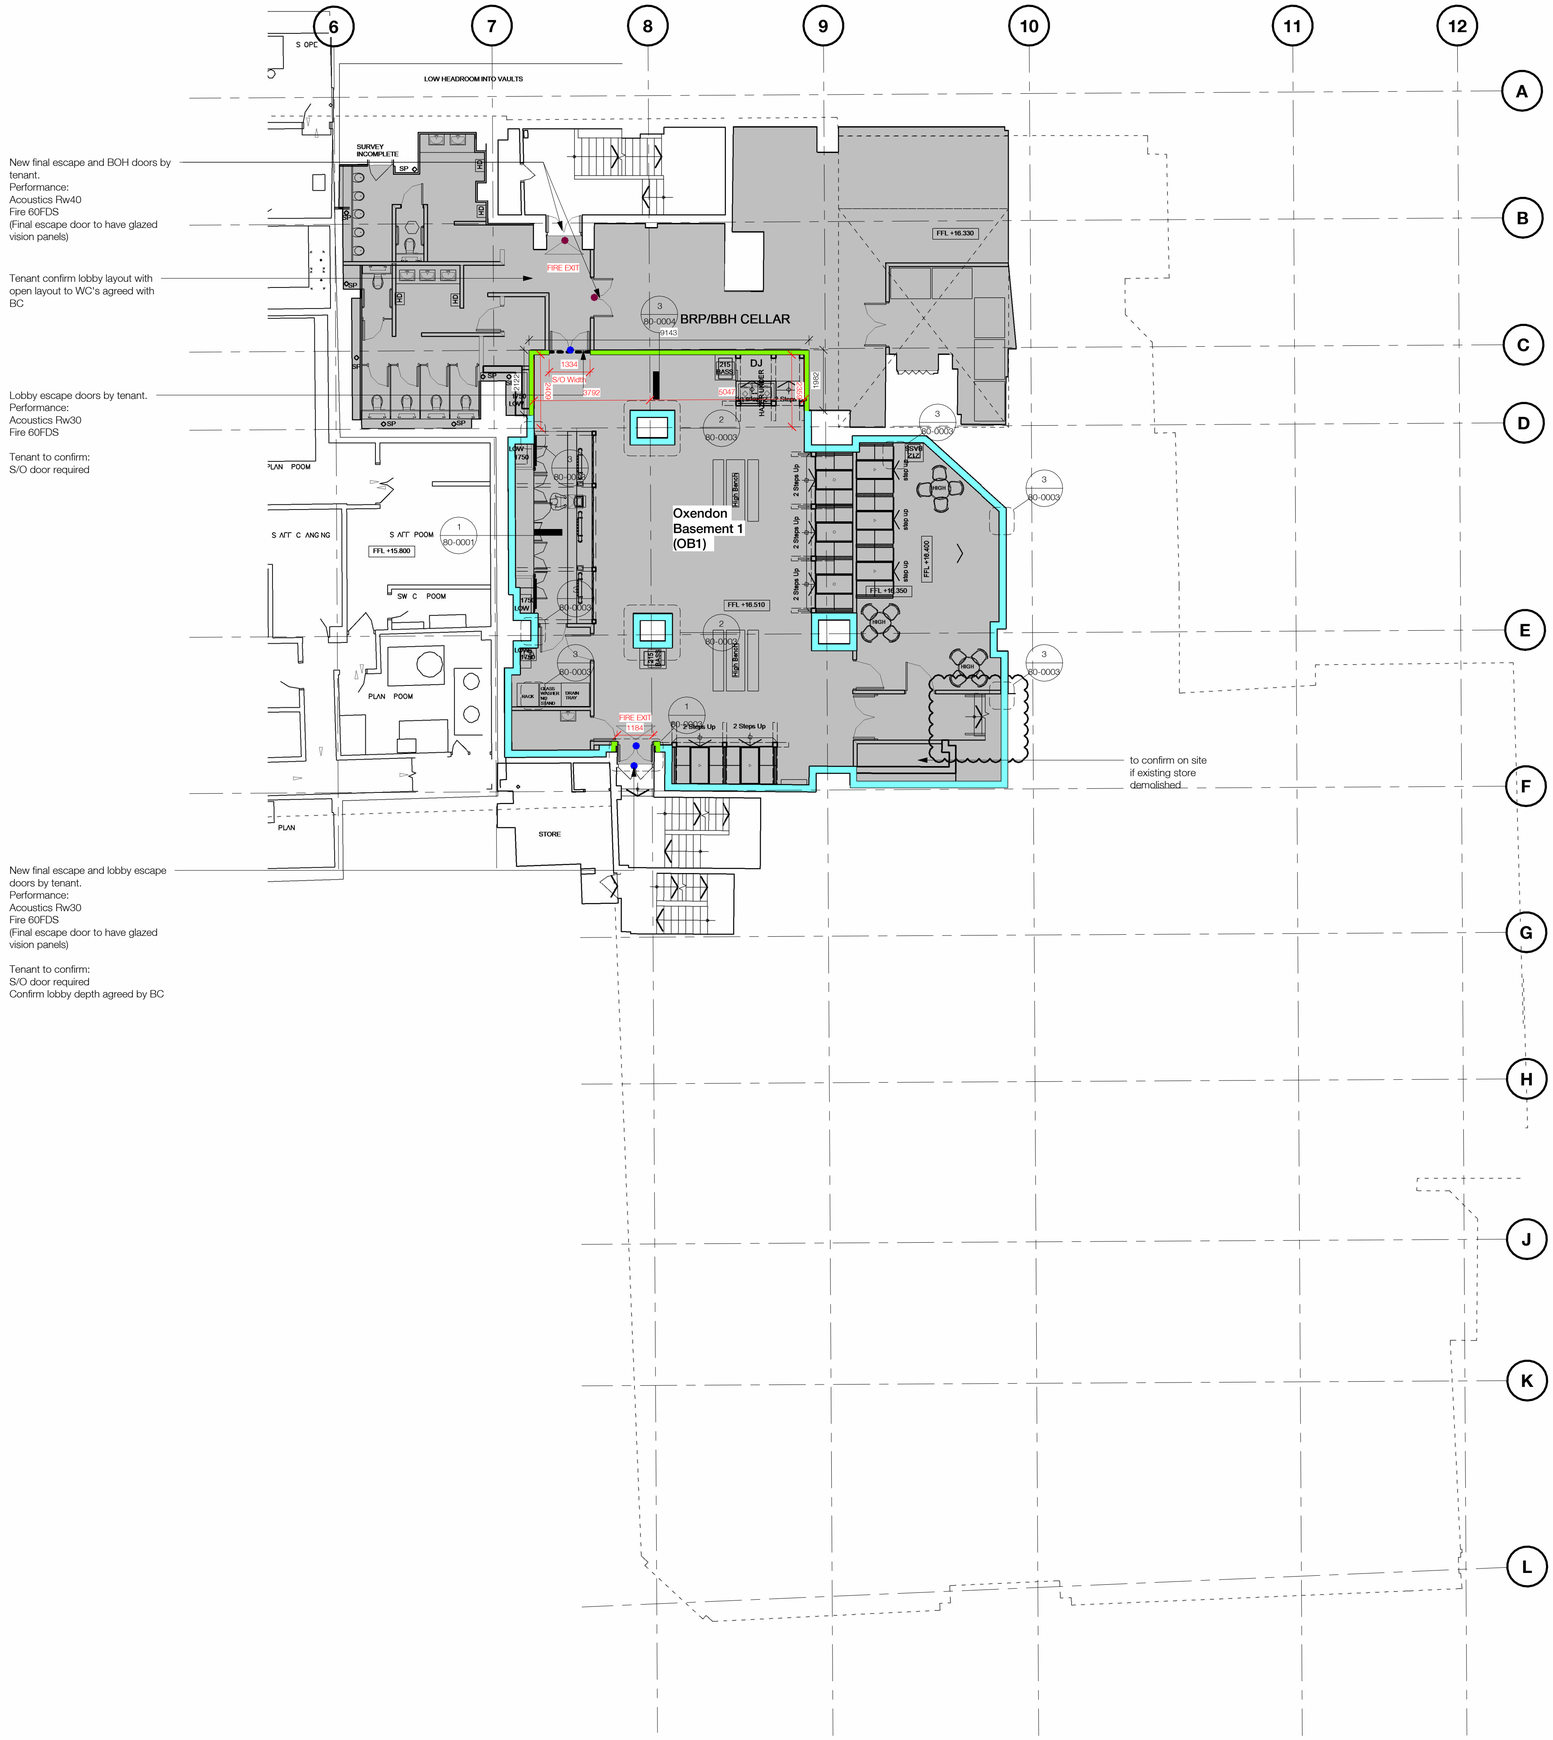

The use of this data by the recipient acts as an agreement of the following statements. Do not use this data if you do not agree with any of the following statements:-

Ryder Architecture has co-ordinated relevant information received from third parties, but are not responsible for the content of the information received from others.

The controlled version of this drawing should be viewed in DWF or PDF format not DWG or other formats. All prints of this drawing must be made in full colour.

Where this drawing has been based upon Ordnance Survey data. Reproduction of this drawing in whole or in part is prohibited without the prior permission of Ordnance Survey.

Do not scale the drawing. Use figured dimensions in all cases. Check all dimensions on site. Report any discrepancies in writing to Ryder before proceeding.

Scale 1:100 (m)

0 1 2 4 8

N

Existing Building Information – Assumptions

The tender information has been prepared in the absence of an internal survey or intrusive surveys to verify the existing building fabric, structural capacity or fire compartment.

Proposals are based on reasonable assumptions typical of buildings of this age and type and are subject to survey verification following strip-out works.

For further detailed layouts refer to tenant proposal drawings.

Legend Wall Types

IWL-1	9s_25_25_45_35 Acoustic rating: NR15 Fire Rating: 90min 146mm I stud, 100mm acoustic insulation, 4#15mm plasterboard.
IWL-2	9s_25_25_45_35 Acoustic rating: NR15 Fire Rating: 90min 92mm I stud, 100mm acoustic insulation, 4#15mm plasterboard.
IWL-3	9s_tbc Acoustic : NR15 Fire Rating: 90min 4#15mm plasterboard.
IWS-1	9s_tbc Acoustic rating NR15 Fire Rating: 90min 2#15mm plasterboard, 92mm I stud, 100mm acoustic insulation, 2#15mm plasterboard.
IWS-2	9s_tbc Acoustic rating tbc Fire Rating: 120min Shaftwall 3#15mm plasterboard, 92mm I stud, 25mm acoustic insulation, 1#30mm coreboard.
BLK-1	9s_tbc Dense Blockwork wall min density 1800kg/m3 140mm thick

Acoustic Door Types

- Rw30
- Rw35
- Rw40

Setting Out - Dims

XX — Dimensions from Gridline. Dimensions to centre line of partitions

XX — Dimension of partition

Rev	Description	Drawn	Checked	Date
C1	Setting out dimensions added for IWS	NCH	JRI	07/10/26
P03	layout change to align with Tenant Frozen layout / omission of all acoustic proposals to HB1 / new tenant riser added / acoustic and fire door performances added	NCH	JRI	07/09/26
P02	Issue for Acoustic Comments	NCH	JRI	01/04/26
P01	First Issue for Information	NCH	JRI	10/02/26

Suitability
Construction Issue

Project
Helios Construction London Limited
Shell and Core Acoustic Works - Ex Tiger Tiger Unit
Haymarket House, 28-29 Haymarket, London

Drawing
Oxendon Basement Level OB1 Proposed Layout


Drawing Number

Project ID	Origin.	Func.	Spatial	Form	Disc.	Number
TIG	- RYD -	00	- 00	- DDR	- A -	10-0099

Project Number	Scale at A1	Status	Revision
11398-01	As indicated	S5	C1

info@ryderarchitecture.com
www.ryderarchitecture.com

Ryder

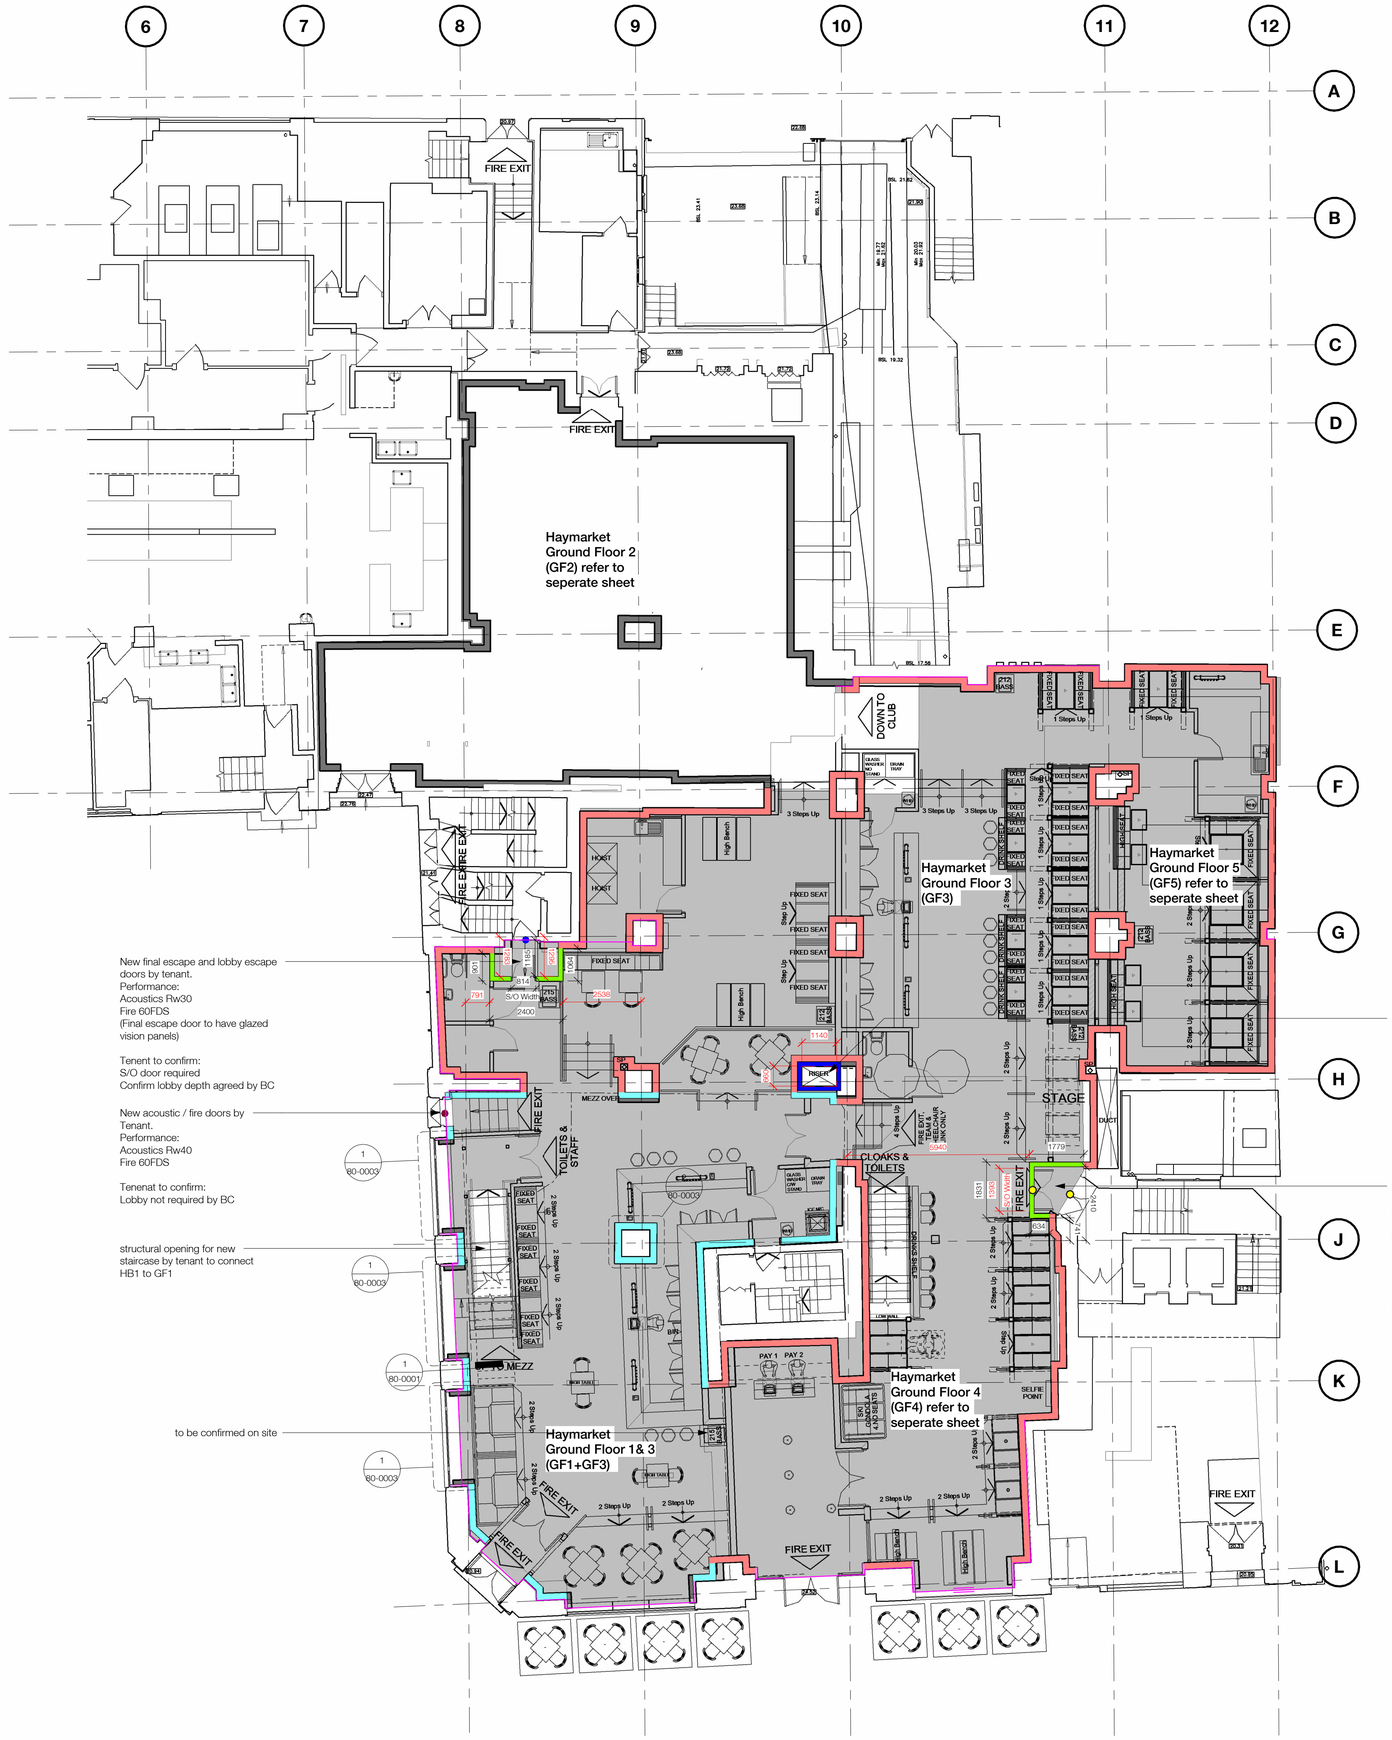

The use of this data by the recipient acts as an agreement of the following statements. Do not use this data if you do not agree with any of the following statements:-

Ryder Architecture has co-ordinated relevant information received from third parties, but are not responsible for the content of the information received from others.

The controlled version of this drawing should be viewed in DWF or PDF format not DWG or other formats. All prints of this drawing must be made in full colour.

Where this drawing has been based upon Ordnance Survey data. Reproduction of this drawing in whole or in part is prohibited without the prior permission of Ordnance Survey.

Do not scale the drawing. Use figured dimensions in all cases. Check all dimensions on site. Report any discrepancies in writing to Ryder before proceeding.

Scale 1:100 (m)

0 1 2 4 8

N

Existing Building Information – Assumptions

The tender information has been prepared in the absence of an internal survey or intrusive surveys to verify the existing building fabric, structural capacity or fire compartment.

Proposals are based on reasonable assumptions typical of buildings of this age and type and are subject to survey verification following strip-out works.

For further detailed layouts refer to tenant proposal drawings.

Legend Wall Types

IWL-1	9s_25_25_45_35 Acoustic rating: NR15 Fire Rating: 90min 146mm I stud, 100mm acoustic insulation, 4#15mm plasterboard.
IWL-2	9s_25_25_45_35 Acoustic rating: NR15 Fire Rating: 90min 92mm I stud, 100mm acoustic insulation, 4#15mm plasterboard.
IWL-3	9s_tbc Acoustic : NR15 Fire Rating: 90min 4#15mm plasterboard.
IWS-1	9s_tbc Acoustic rating NR15 Fire Rating: 90min 2#15mm plasterboard, 92mm I stud, 100mm acoustic insulation, 2#15mm plasterboard.
IWS-2	9s_tbc Acoustic rating tbc Fire Rating: 120min Shaftwall 3#15mm plasterboard, 92mm I stud, 25mm acoustic insulation, 1#30mm coreboard.
BLK-1	9s_tbc Dense Blockwork wall min density 1800kg/m3 140mm thick

Acoustic Door Types

- Rw30
- Rw35
- Rw40

Setting Out - Dims

XX — Dimensions from Gridline. Dimensions to centre line of partitions

XX — Dimension of partition

Rev	Description	Drawn	Checked	Date
C1	Setting out dimensions added for IWS	NCH	JRI	07/10/26
P03	layout change to align with Tenant Frozen layout / omission of all acoustic proposals to HB1 / new tenant riser added / acoustic and fire door performances added	NCH	JRI	07/09/26
P02	Issue for Acoustic Comments	NCH	JRI	01/04/26
P01	First Issue for Information	NCH	JRI	10/02/26

Suitability
Construction Issue

Project
Helios Construction London Limited
Shell and Core Acoustic Works - Ex Tiger Tiger Unit
Haymarket House, 28-29 Haymarket, London

Drawing
Ground Floor Levels GF1 & GF3 Proposed Layout

Drawing Number

Project ID	Origin	Func.	Spatial	Form	Disc.	Number
TIG	- RYD -	00	- 00 -	DDR	- A -	10-0102

Project Number	Scale at A1	Status	Revision
11398-01	As indicated	S5	C1

info@ryderarchitecture.com
www.ryderarchitecture.com
Ryder

The use of this data by the recipient acts as an agreement of the following statements. Do not use this data if you do not agree with any of the following statements:-

Ryder Architecture has co-ordinated relevant information received from third parties, but are not responsible for the content of the information received from others.

The controlled version of this drawing should be viewed in DWF or PDF format not DWG or other formats. All prints of this drawing must be made in full colour.

Where this drawing has been based upon Ordnance Survey data. Reproduction of this drawing in whole or in part is prohibited without the prior permission of Ordnance Survey.

Do not scale the drawing. Use figured dimensions in all cases. Check all dimensions on site. Report any discrepancies in writing to Ryder before proceeding.

Scale 1:100 (m)

0 1 2 4 8

N



Existing Building Information – Assumptions

The tender information has been prepared in the absence of an internal survey or intrusive surveys to verify the existing building fabric, structural capacity or fire compartment.

Proposals are based on reasonable assumptions typical of buildings of this age and type and are subject to survey verification following strip-out works.

For further detailed layouts refer to tenant proposal drawings.

Legend Wall Types

IWL-1
Ss_25_25_45_35
Acoustic rating: NR15
Fire Rating: 90min
146mm I stud, 100mm acoustic insulation, 4#15mm plasterboard.

IWL-2
Ss_25_25_45_35
Acoustic rating: NR15
Fire Rating: 90min
92mm I stud, 100mm acoustic insulation, 4#15mm plasterboard.

IWL-3
Ss_tbc
Acoustic : NR15
Fire Rating: 90min
4#15mm plasterboard.

IWS-1
Ss_tbc
Acoustic rating NR15
Fire Rating: 90min
2#15mm plasterboard, 92mm I stud, 100mm acoustic insulation, 2#15mm plasterboard.

IWS-2
Ss_tbc
Acoustic rating tbc
Fire Rating: 120min
Shaftwall 3#15mm plasterboard, 92mm I stud, 25mm acoustic insulation, 1#30mm coreboard.

BLK-1
Ss_tbc
Dense Blockwork wall
min density 1800kg/m3
140mm thick

Acoustic Door Types

Rw30

Rw35

Rw40

Setting Out - Dims

XX — Dimensions from Gridline. Dimensions to centre line of partitions

XX — Dimension of partition

Rev	Description	Drawn	Checked	Date
C1	Setting out dimensions added for IWS	NCH	JRI	07/10/26
P04	layout change to align with Tenant Frozen layout / omission of all acoustic proposals to HB1 / new tenant riser added / acoustic and fire door performances added	NCH	JRI	07/09/26
P03	Issue for Acoustic Comments	NCH	JRI	01/04/26
P02	General update	NCH	JRI	24/03/26
P01	First Issue for Information	NCH	JRI	10/02/26

Suitability
Construction Issue

Project
Helios Construction London Limited
Shell and Core Acoustic Works - Ex Tiger Tiger Unit
Haymarket House, 28-29 Haymarket, London

Drawing
Mezzanine Level MO1 Proposed Layout

Drawing Number

Project ID	Origin.	Func.	Spatial	Form	Disc.	Number
TIG	- RYD -	00	- 00 -	DDR	- A -	10-0103

Project Number	Scale at	Status	Revision
11398-01	As indicated	S5	C1

info@ryderarchitecture.com
www.ryderarchitecture.com

Ryder